


(150' WIDE)

(150' WIDE)

SALE AVENUE (60' WIDE)

AMSTERDAM AVENUE (100' WIDE)

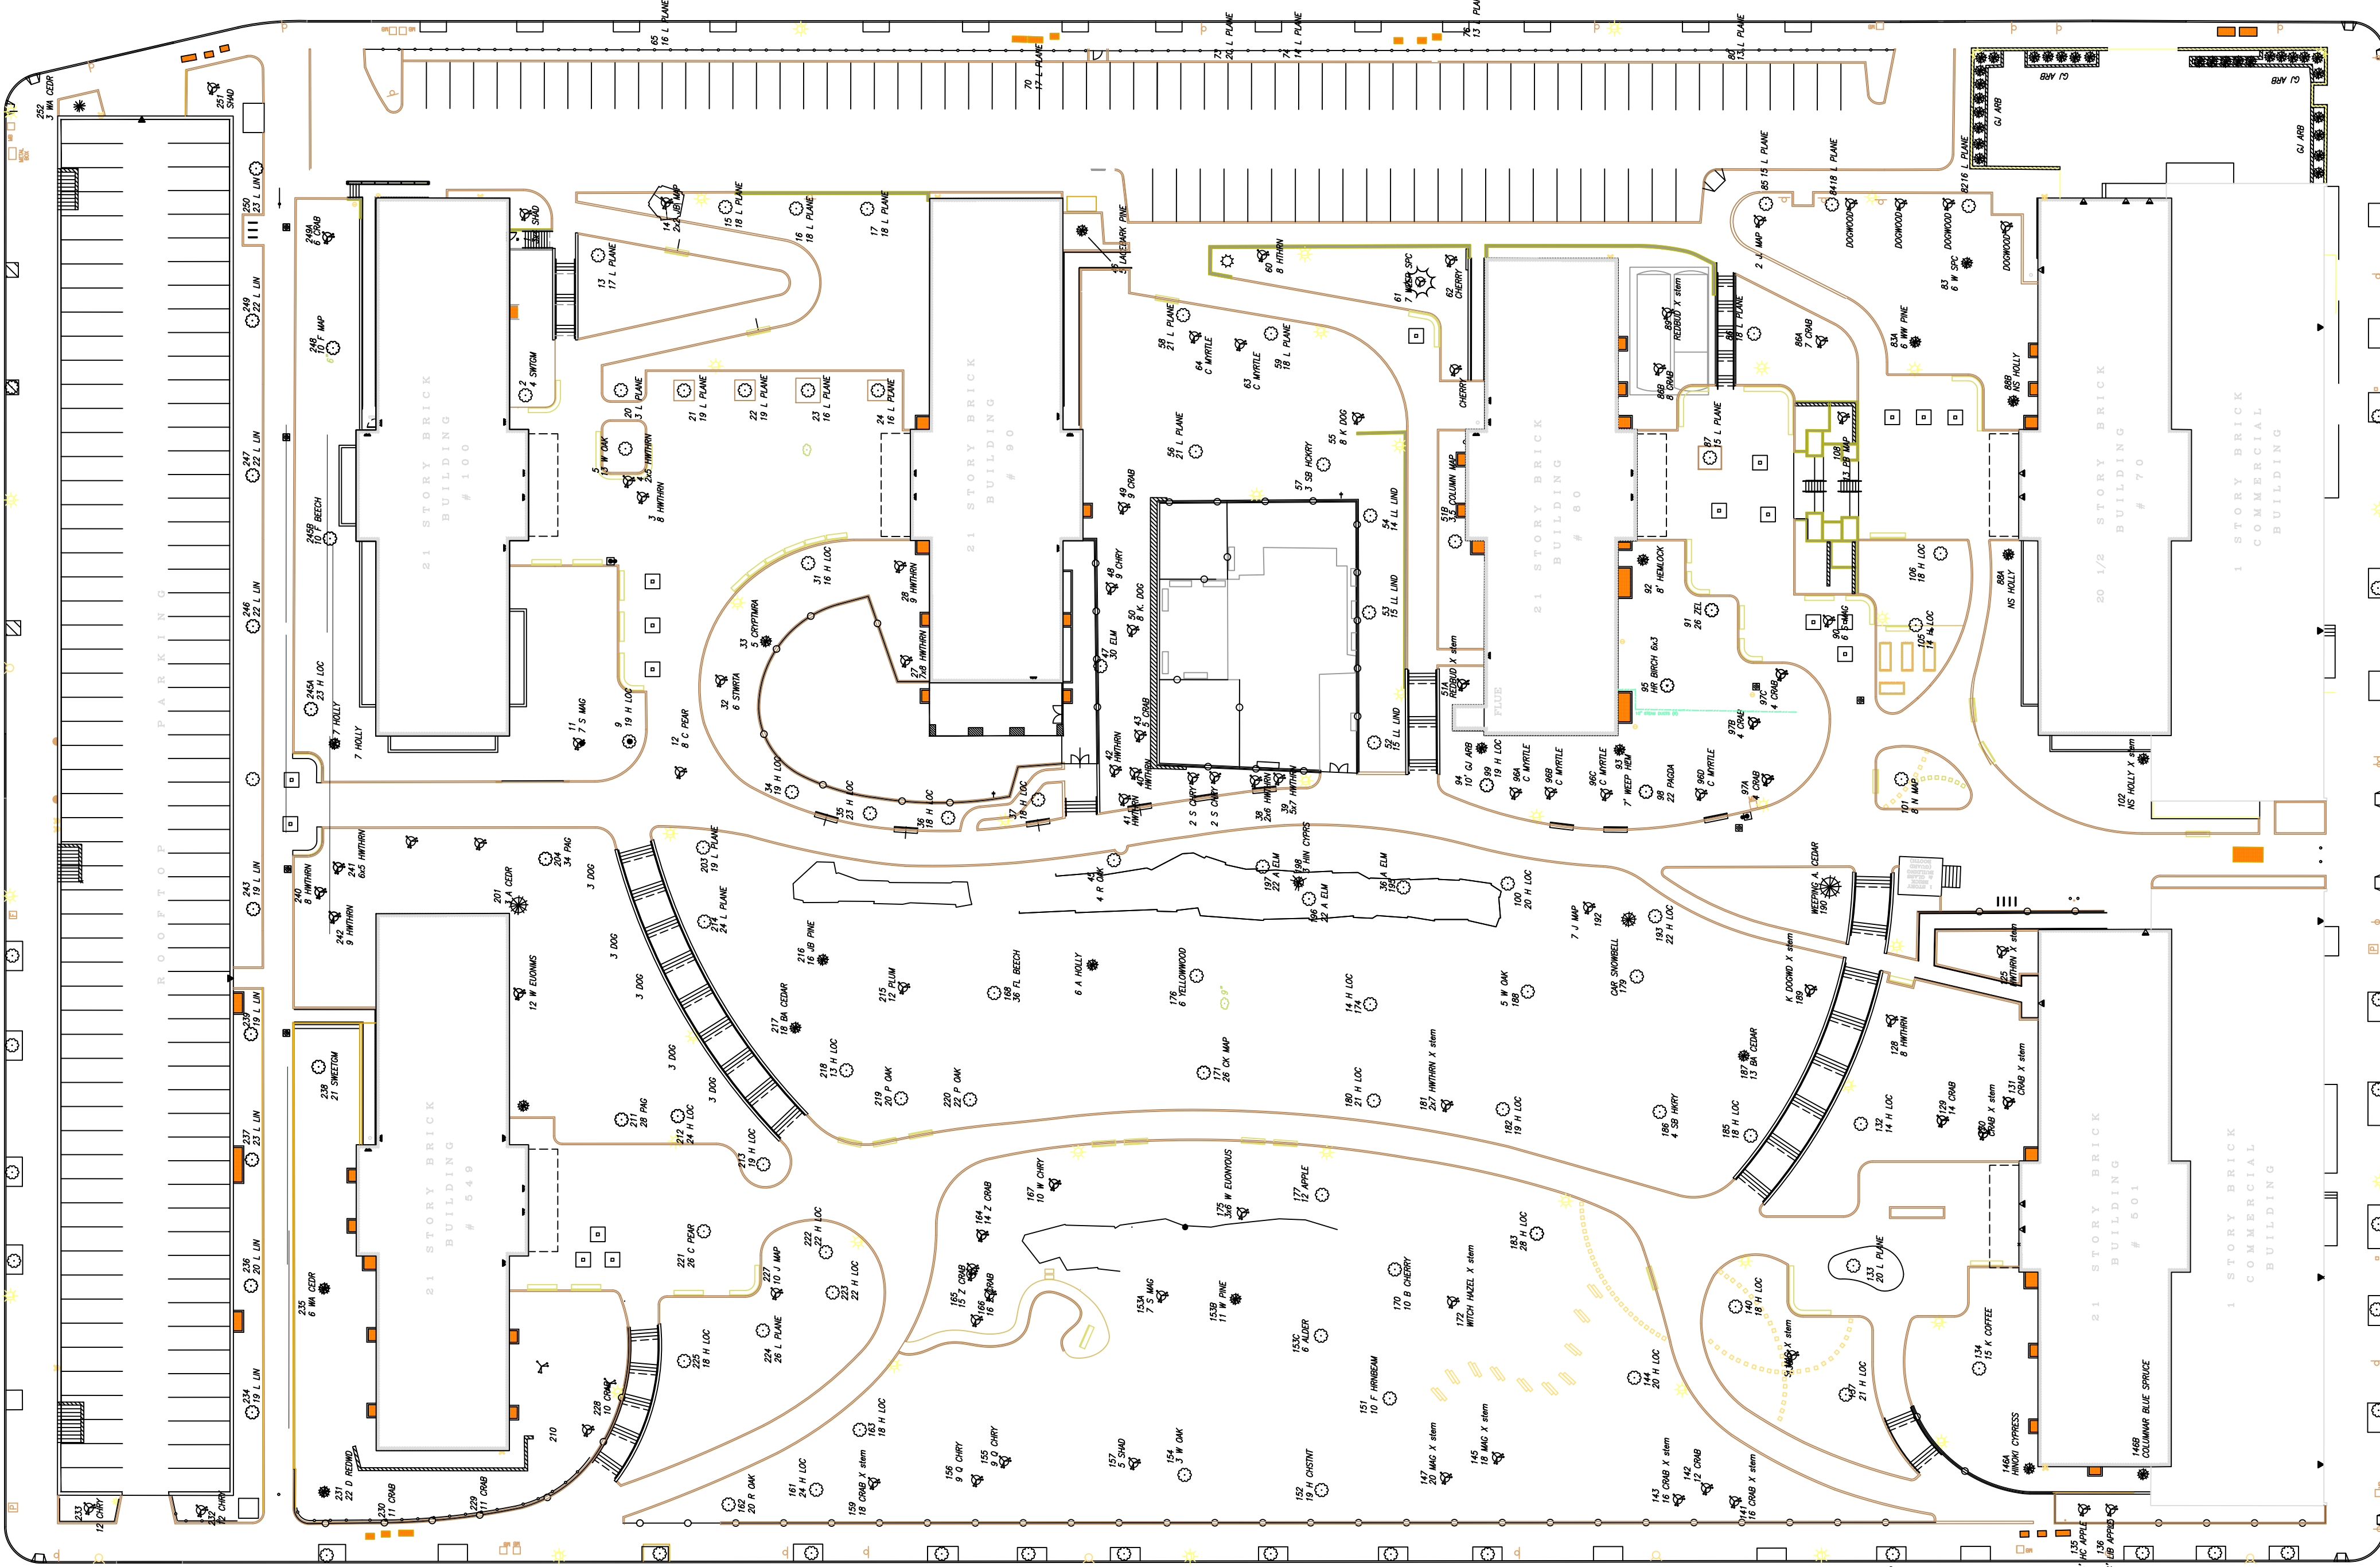

WEST 1ST STREET (60' WIDE)

WEST 3RD STREET (60' WIDE)